
Massenermittlung

VERMESSUNG DIERING

Dipl. Ing. Frank Diering
Vermessungsingenieur
Lindenstraße 28
15230 Frankfurt (Oder)

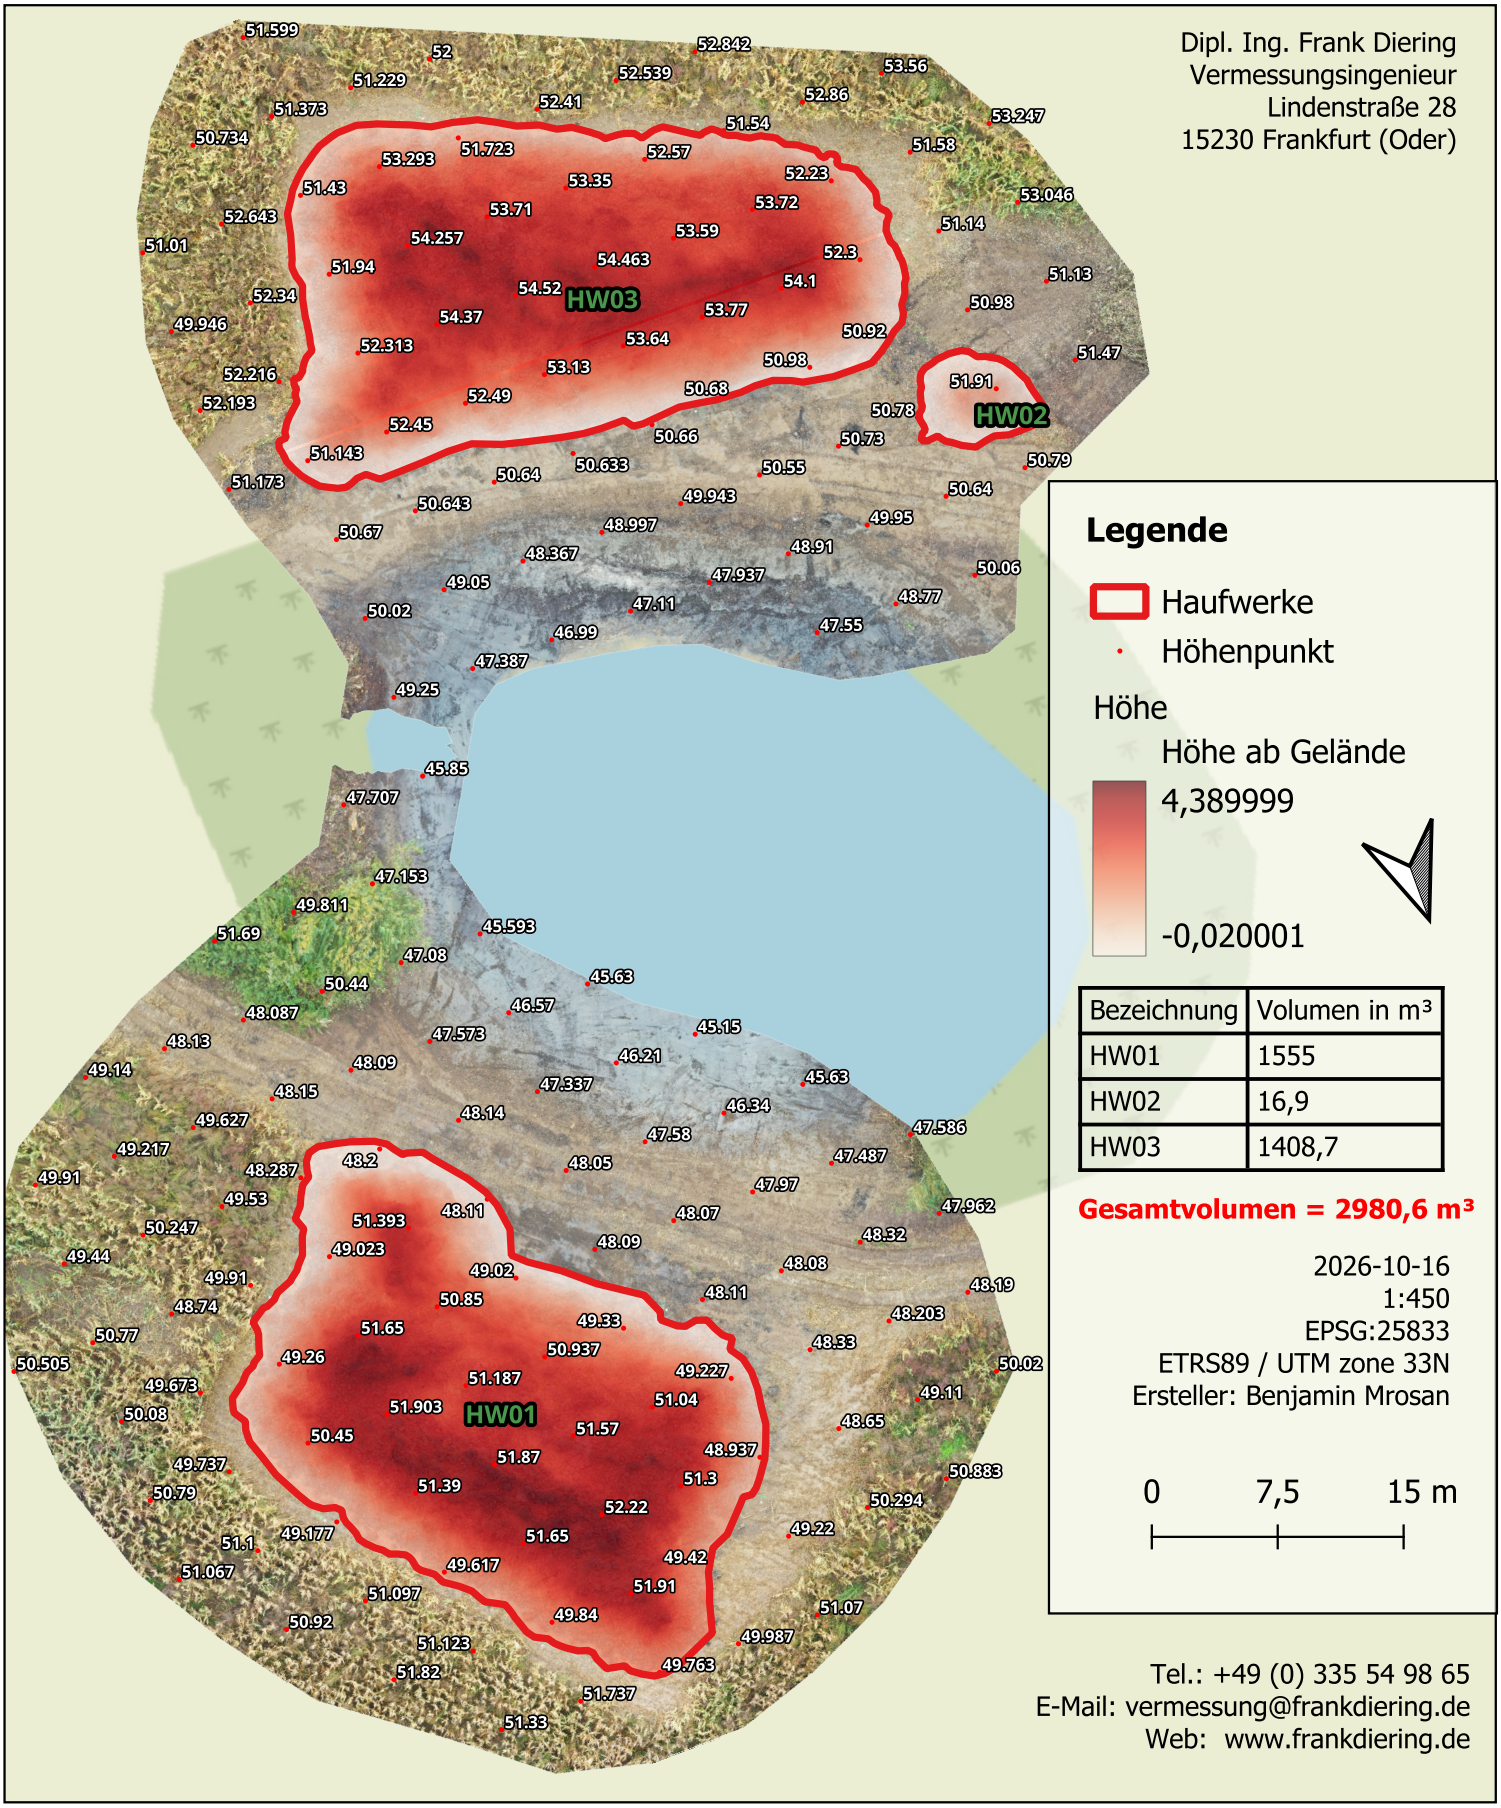

Legende

Haufwerke

Höhenpunkt

Höhe

Höhe ab Gelände

4,389999

-0,020001

Bezeichnung	Volumen in m³
HW01	1555
HW02	16,9
HW03	1408,7

Gesamtvolumen = 2980,6 m³

2026-10-16
1:450
EPSG:25833
ETRS89 / UTM zone 33N
Ersteller: Benjamin Mrosan

0 7,5 15 m

Tel.: +49 (0) 335 54 98 65
E-Mail: vermessung@frankdiering.de
Web: www.frankdiering.de